
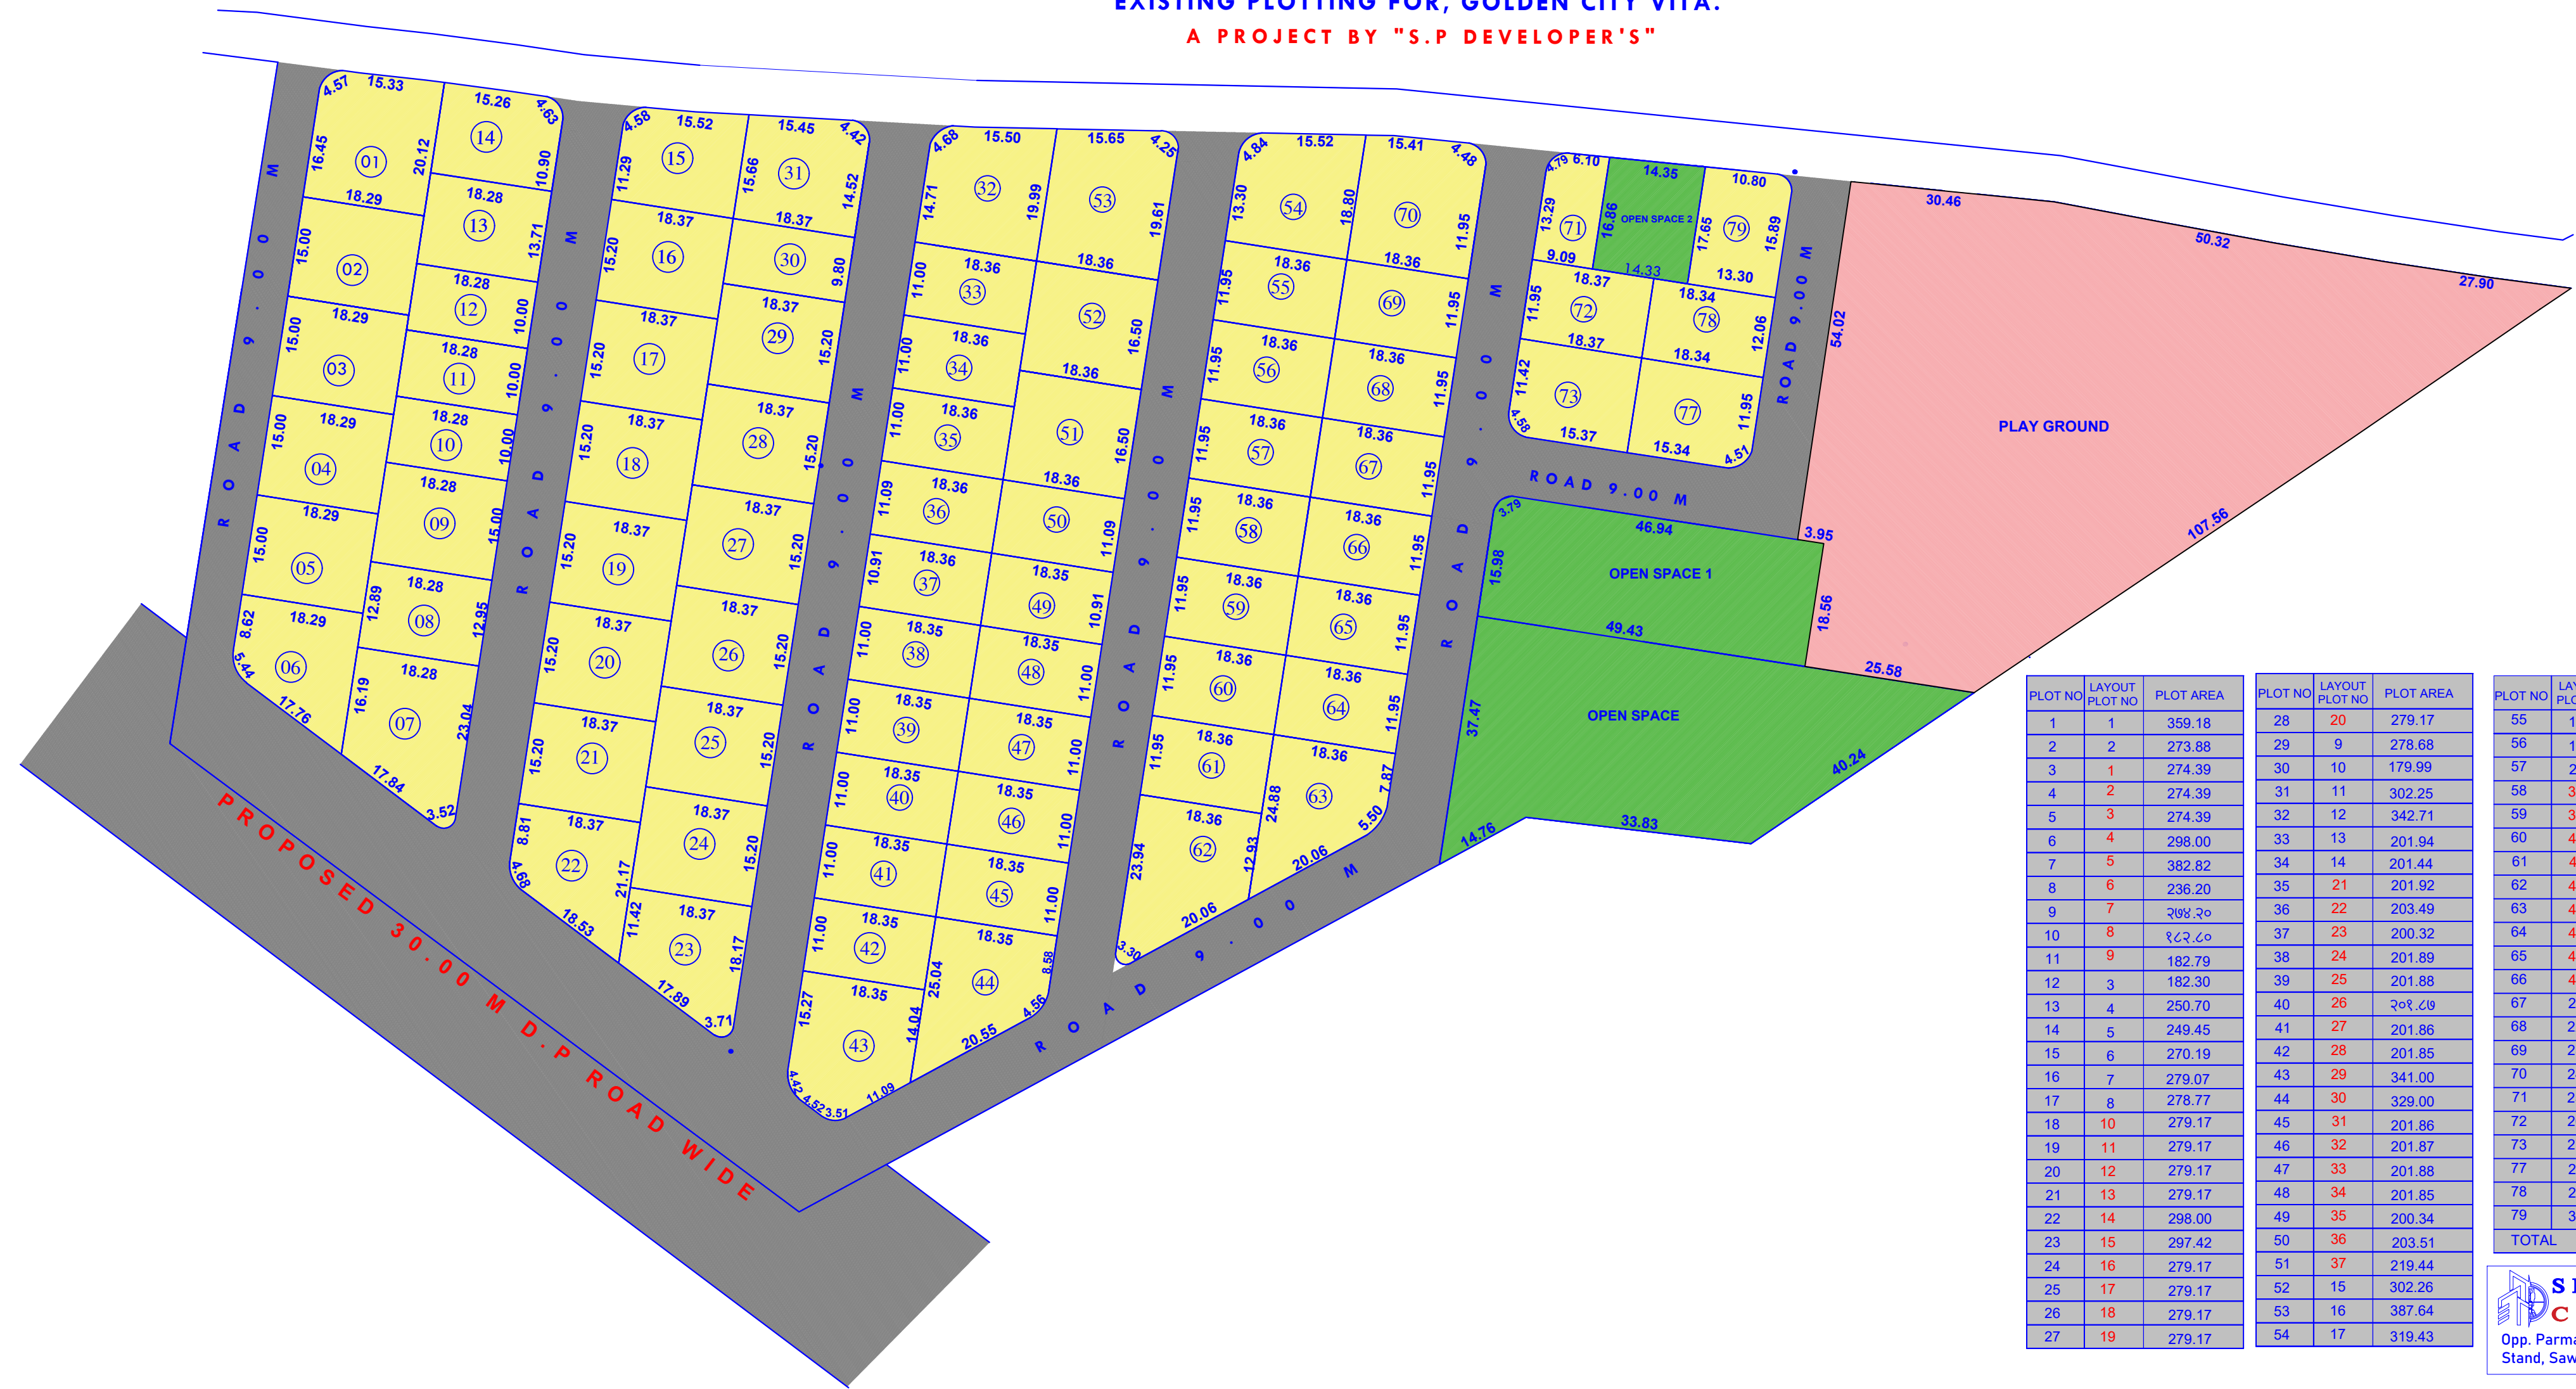


EXISTING PLOTTING FOR, GOLDEN CITY VITA.
A PROJECT BY "S.P DEVELOPER'S"

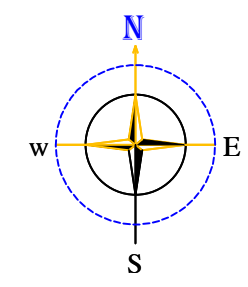

PLOT NO	LAYOUT PLOT NO	PLOT AREA	PLOT NO	LAYOUT PLOT NO	PLOT AREA	PLOT NO	LAYOUT PLOT NO	PLOT AREA
1	1	359.18	28	20	279.17	55	18	219.46
2	2	273.88	29	9	278.68	56	19	219.42
3	1	274.39	30	10	179.99	57	20	218.94
4	2	274.39	31	11	302.25	58	38	219.44
5	3	274.39	32	12	342.71	59	39	219.45
6	4	298.00	33	13	201.94	60	40	219.46
7	5	382.82	34	14	201.44	61	41	219.47
8	6	236.20	35	21	201.92	62	42	364.01
9	7	208.20	36	22	203.49	63	43	326.22
10	8	162.60	37	23	200.32	64	44	219.46
11	9	182.79	38	24	201.89	65	45	219.45
12	3	182.30	39	25	201.88	66	46	219.44
13	4	250.70	40	26	201.89	67	21	218.94
14	5	249.45	41	27	201.86	68	22	219.42
15	6	270.19	42	28	201.85	69	23	219.46
16	7	279.07	43	29	341.00	70	24	357.29
17	8	278.77	44	30	329.00	71	25	148.69
18	10	279.17	45	31	201.86	72	26	219.95
19	11	279.17	46	32	201.87	73	27	260.79
20	12	279.17	47	33	201.88	77	28	257.33
21	13	279.17	48	34	201.85	78	29	220.69
22	14	298.00	49	35	200.34	79	30	238.68
23	15	297.42	50	36	203.51	TOTAL		19292.44
24	16	279.17	51	37	219.44			
25	17	279.17	52	15	302.26			
26	18	279.17	53	16	387.64			
27	19	279.17	54	17	319.43			